
Kreuzung Gießerstraße / Naumburger Straße, Leipzig-Plagwitz

Eintragsplan Bestand · Gesamtplan · Maßstab 1:400 bei Druck auf A3 · Raster 10 m · Stand 18.10.2026 · Seite 1 von 2

Verbesserungen bitte farbig einzeichnen (rot oder grün), jede Idee mit einer Nummer im Kreis, darunter kurz beschreiben. Passmarken in den Ecken nicht abdecken. Foto möglichst gerade von oben.

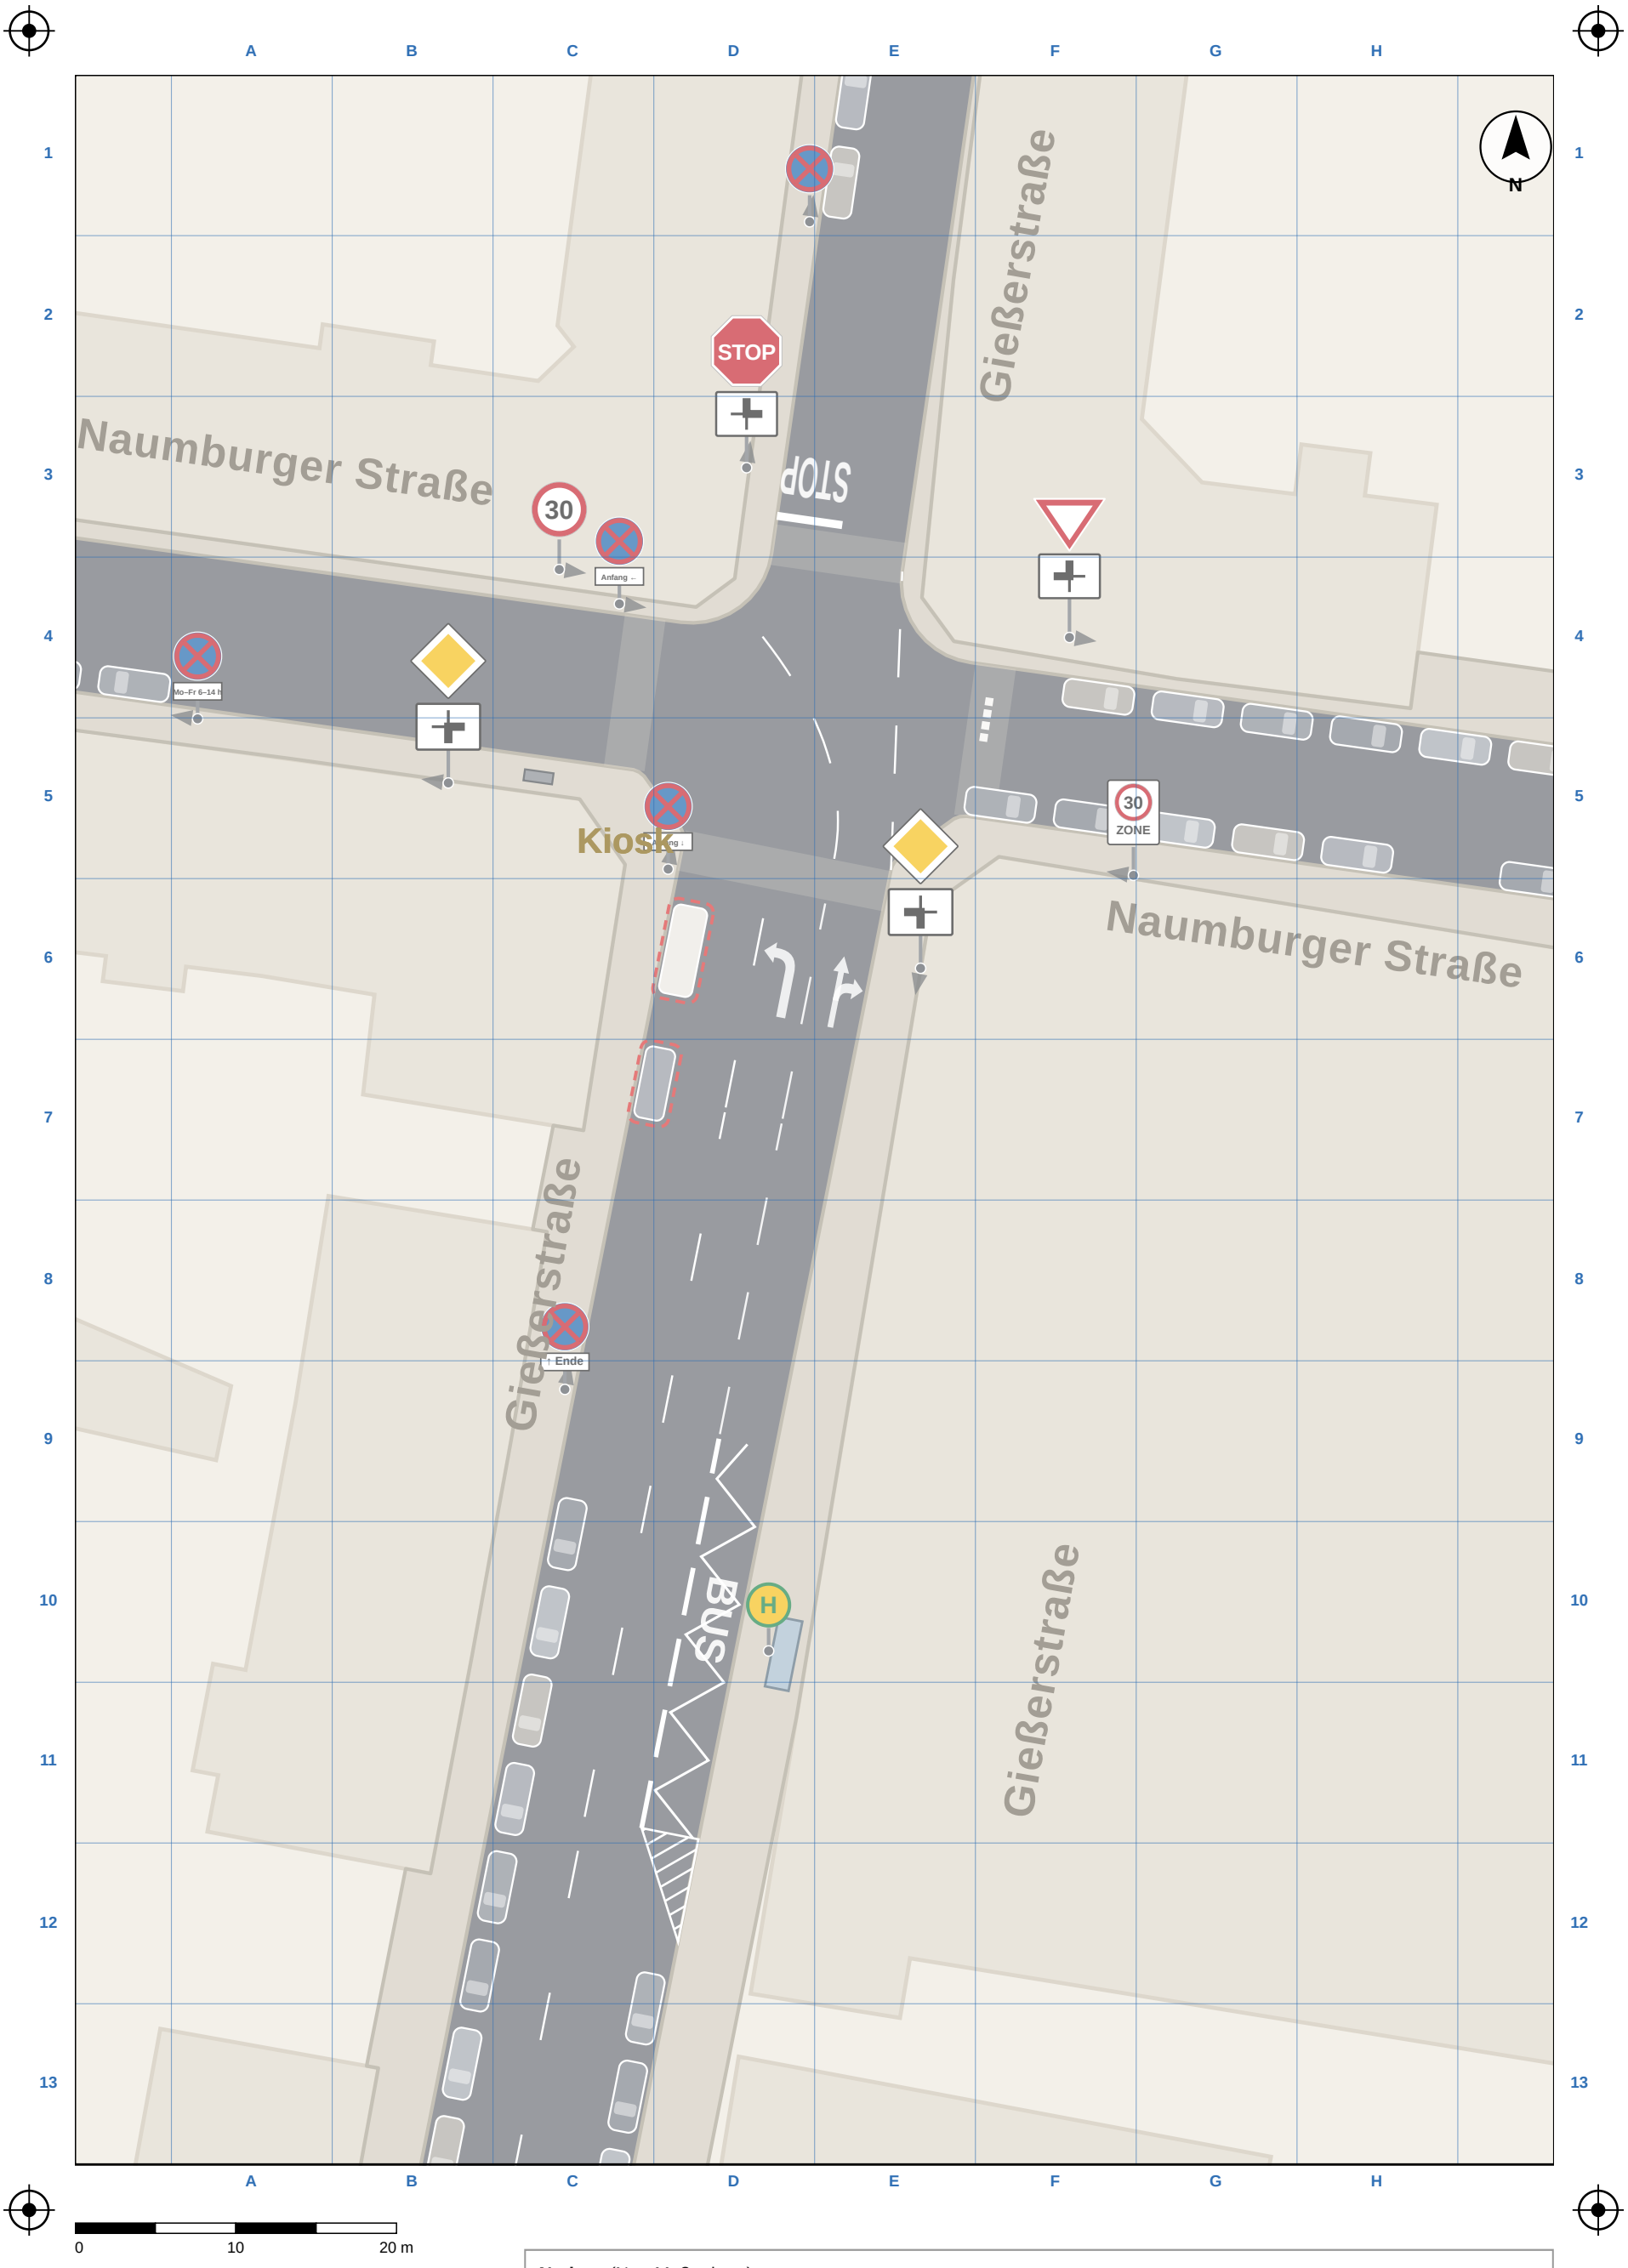


Notizen (Nr. · Maßnahme)

Kreuzung Gießerstraße / Naumburger Straße, Leipzig-Plagwitz

Eintragsplan Bestand · Knoten im Detail · Maßstab 1:200 bei Druck auf A3 · Raster 5 m · Stand 18.10.2026 · Seite 2 von 2

Verbesserungen bitte farbig einzeichnen (rot oder grün), jede Idee mit einer Nummer im Kreis, darunter kurz beschreiben. Passmarken in den Ecken nicht abdecken. Foto möglichst gerade von oben.

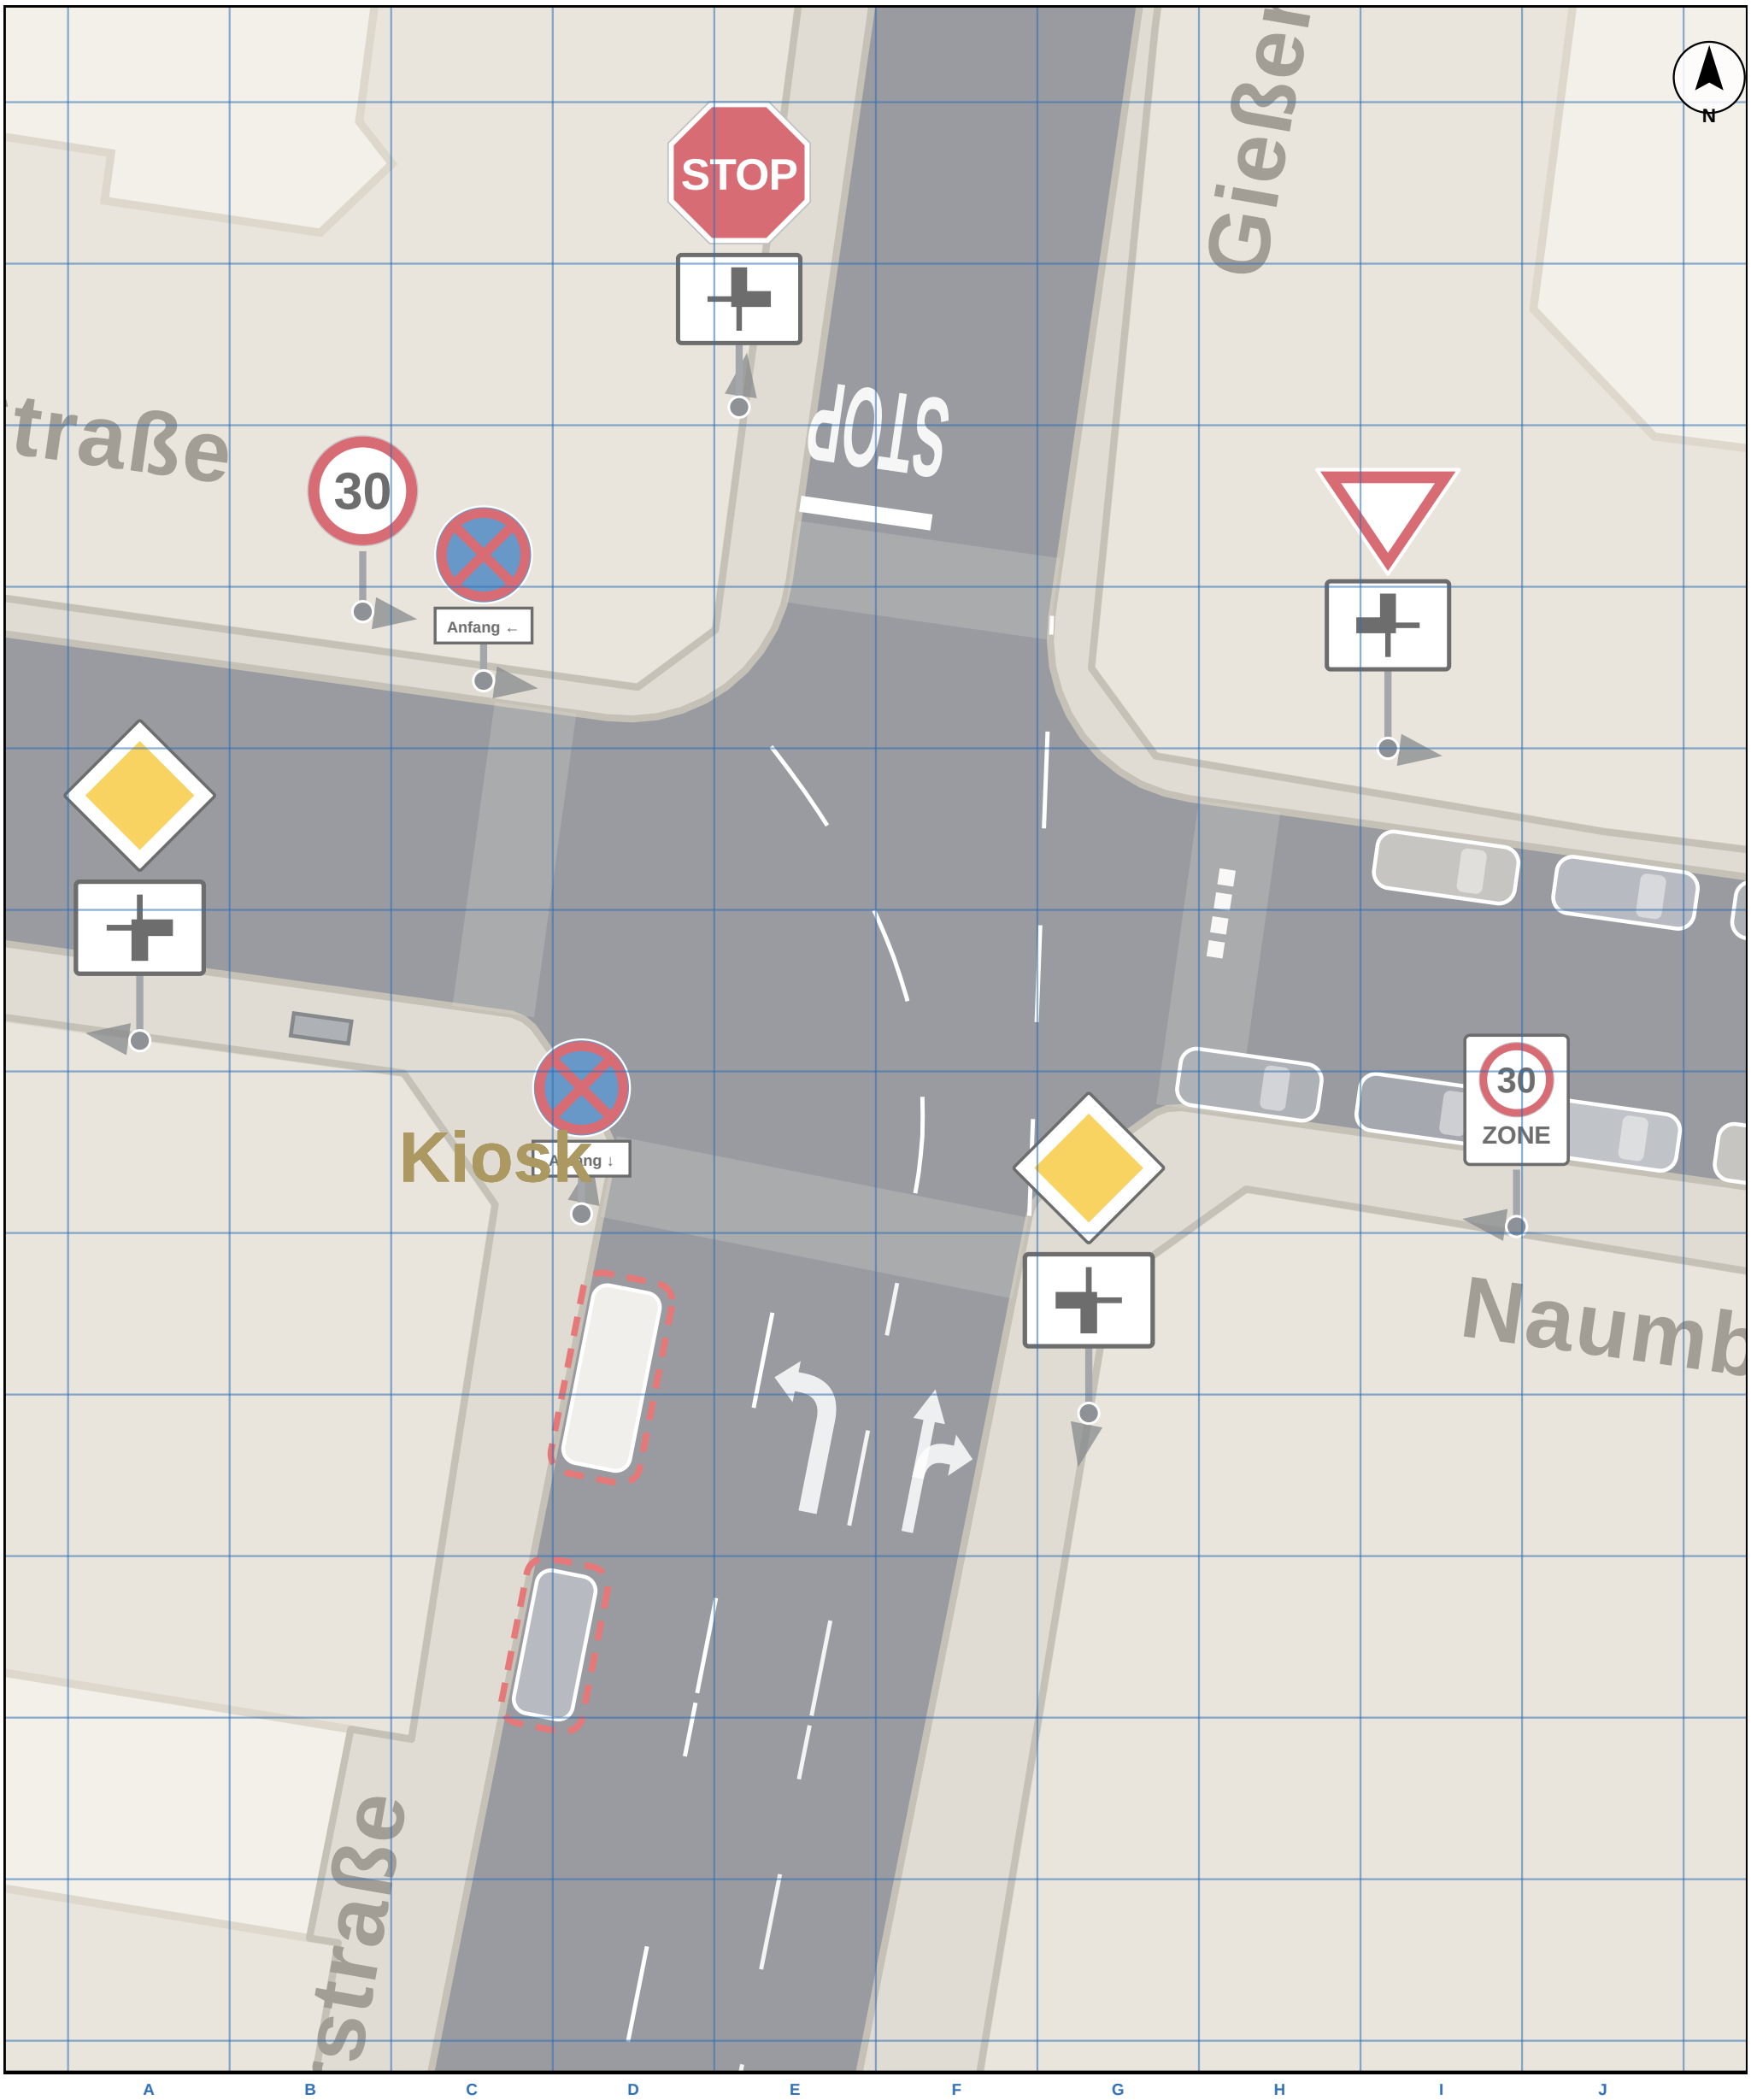

0 5 10 m

Notizen (Nr. · Maßnahme)