
Kreuzung Gießerstraße / Naumburger Straße, Leipzig-Plagwitz

Vorschlag 2 · Gesamtplan · Maßstab 1:400 bei Druck auf A3 · Raster 10 m · Stand 18.10.2026 · Seite 1 von 2

Zwei Kfz-Spuren nach Norden, Rad nach West in Mittellage. Rot = Radverkehr, orange = Rad links abbiegen West nach Nord. Ergänzungen bitte farbig einzeichnen.

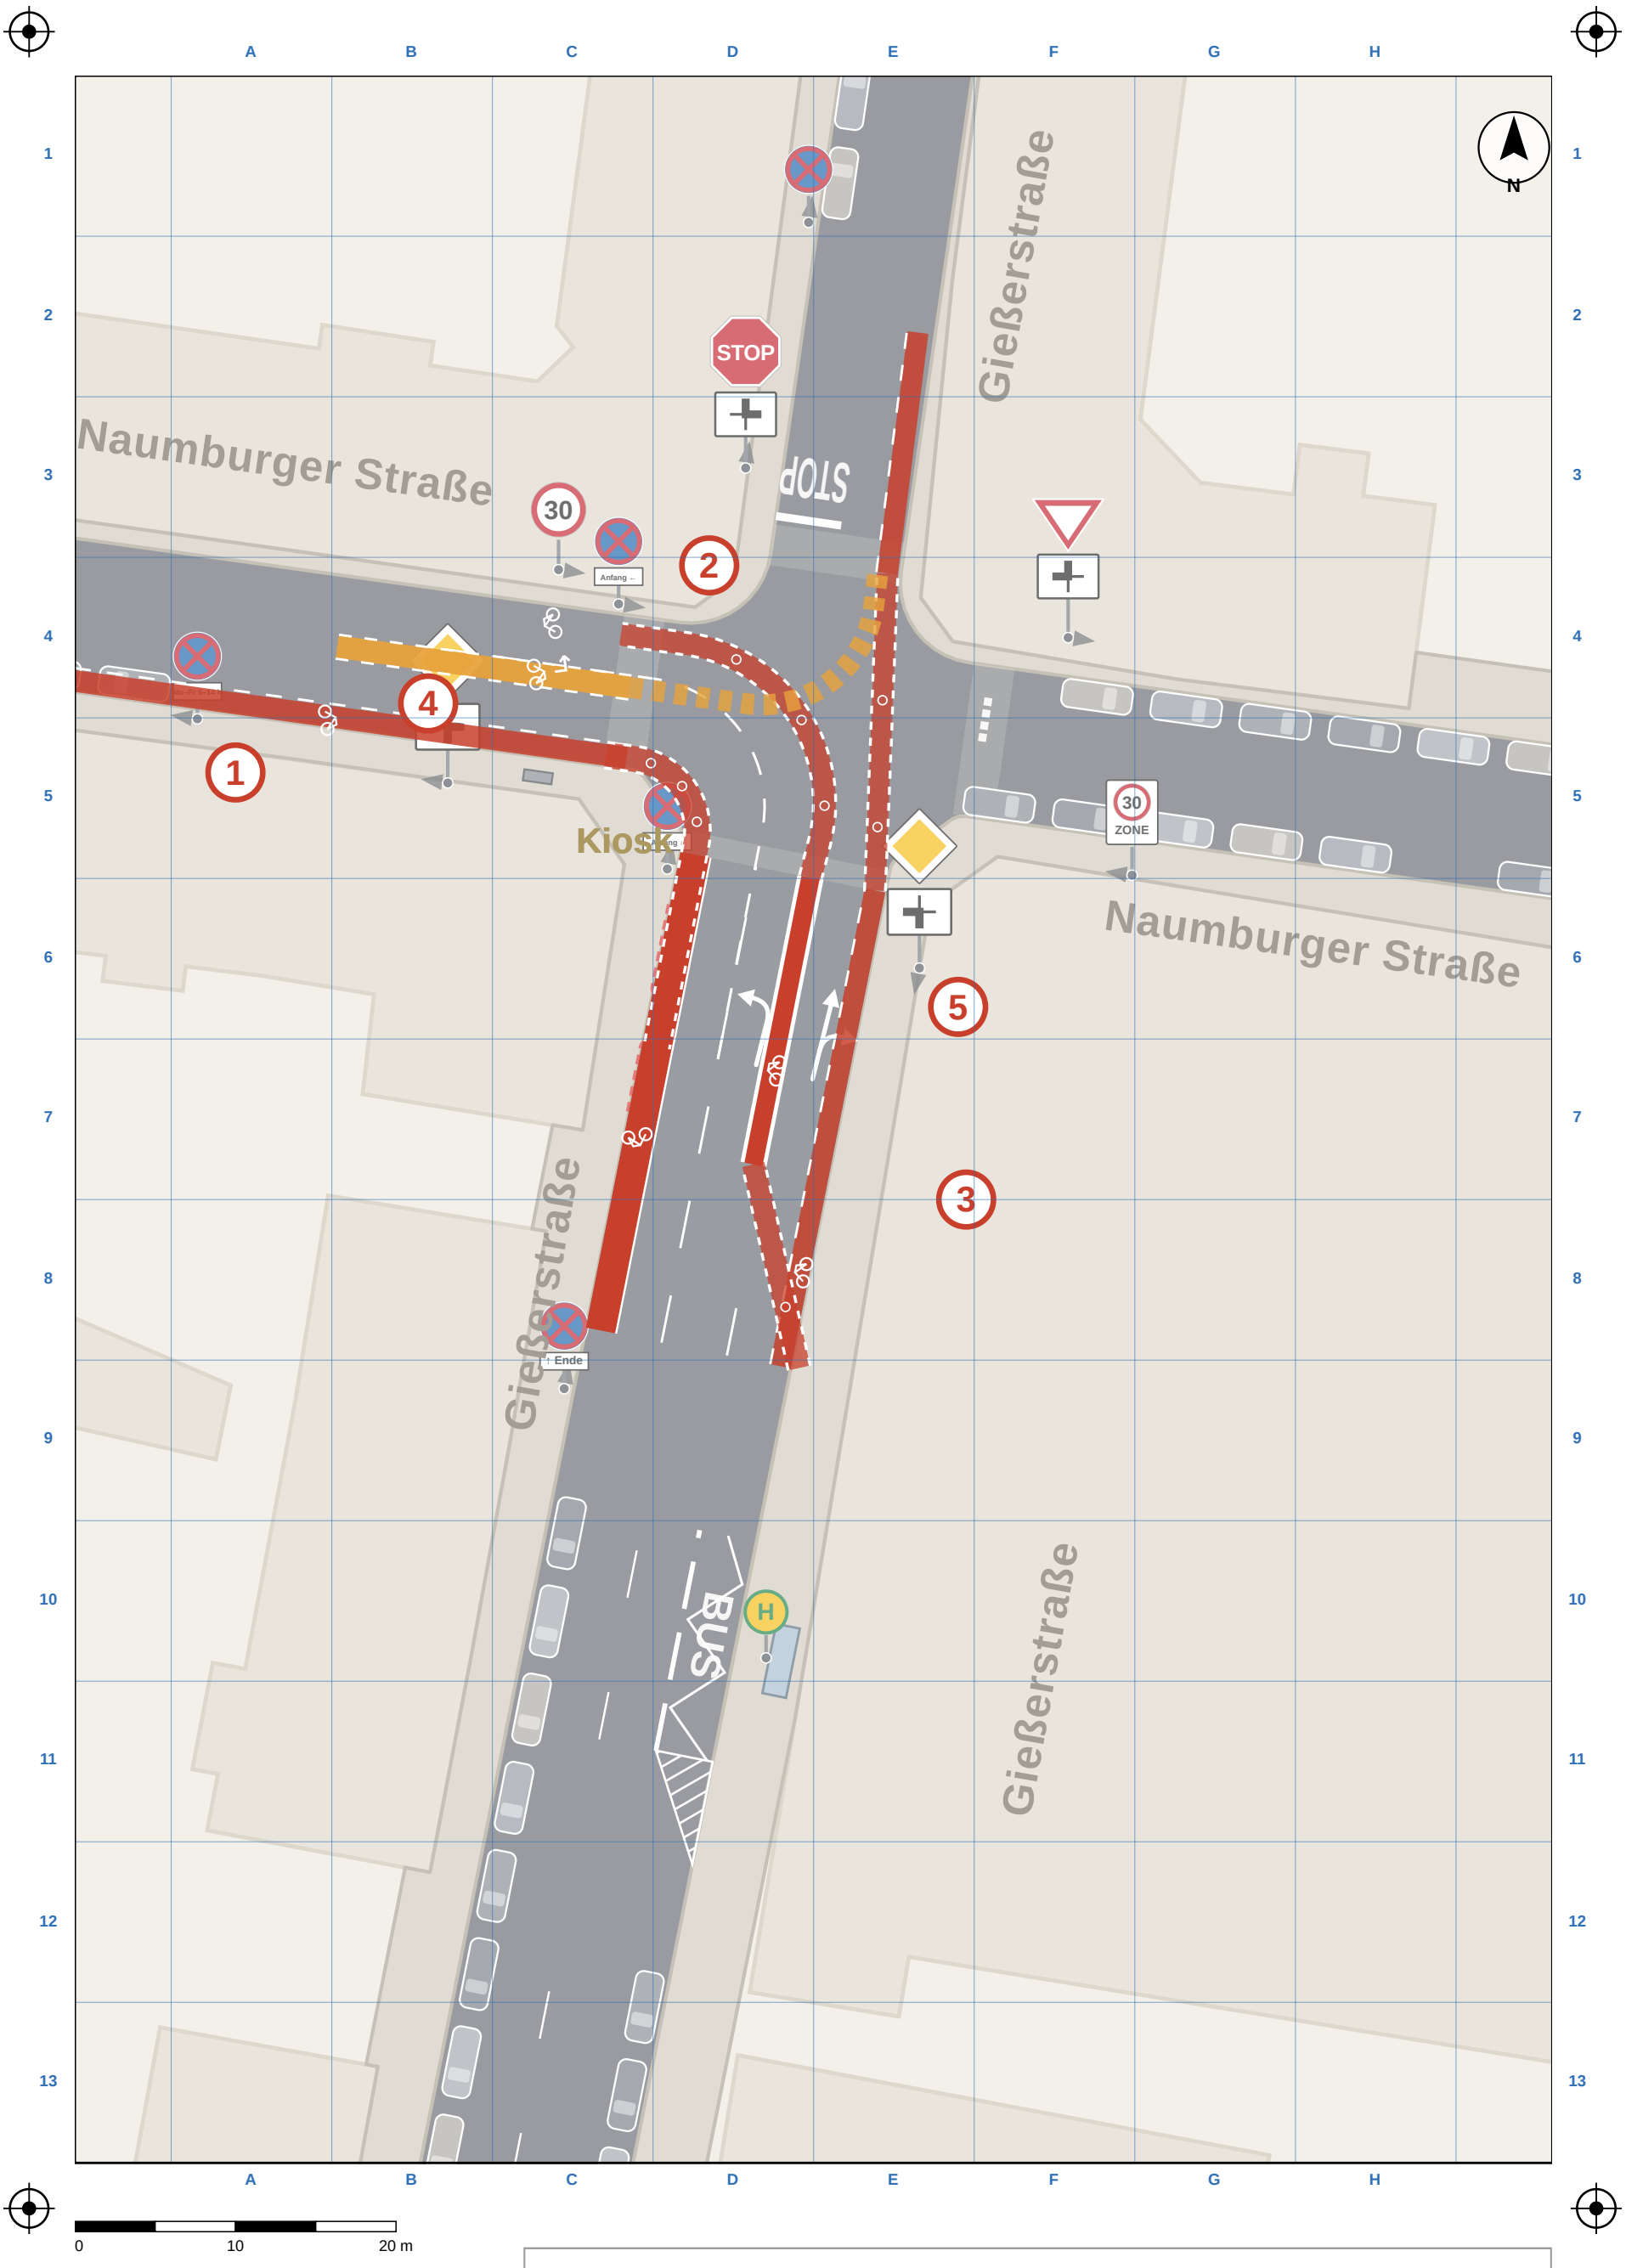


Vorschlag 2 (Weiterentwicklung von Vorschlag 1 nach der Simulation, Lage ca. ±0,5 m)
1 wie Vorschlag 1: Schutzstreifen West ostwärts, Furt um die Kiosk-Ecke, Radfahrstreifen Süd südwärts
2 Rad Süd nach West im Radstreifen in Mittellage, im Bogen rechts neben den abbiegenden Kfz, danach Mischverkehr Tempo 30 · Rad Süd nach Nord rechts, Furt geradeaus
3 Einfädelung: Rad nach West wechselt früh und markiert in die Mittellage · 4 Aufstellstreifen Rad West nach Nord
5 zwei Kfz-Spuren nach Norden bleiben (links / geradeaus und rechts), schmaler: 2,75 m, Mittellage 1,4 m, Schutzstreifen 1,3 m

Kreuzung Gießerstraße / Naumburger Straße, Leipzig-Plagwitz

Vorschlag 2 · Knoten im Detail · Maßstab 1:200 bei Druck auf A3 · Raster 5 m · Stand 18.10.2026 · Seite 2 von 2

Zwei Kfz-Spuren nach Norden, Rad nach West in Mittellage. Rot = Radverkehr, orange = Rad links abbiegen West nach Nord. Ergänzungen bitte farbig einzeichnen.

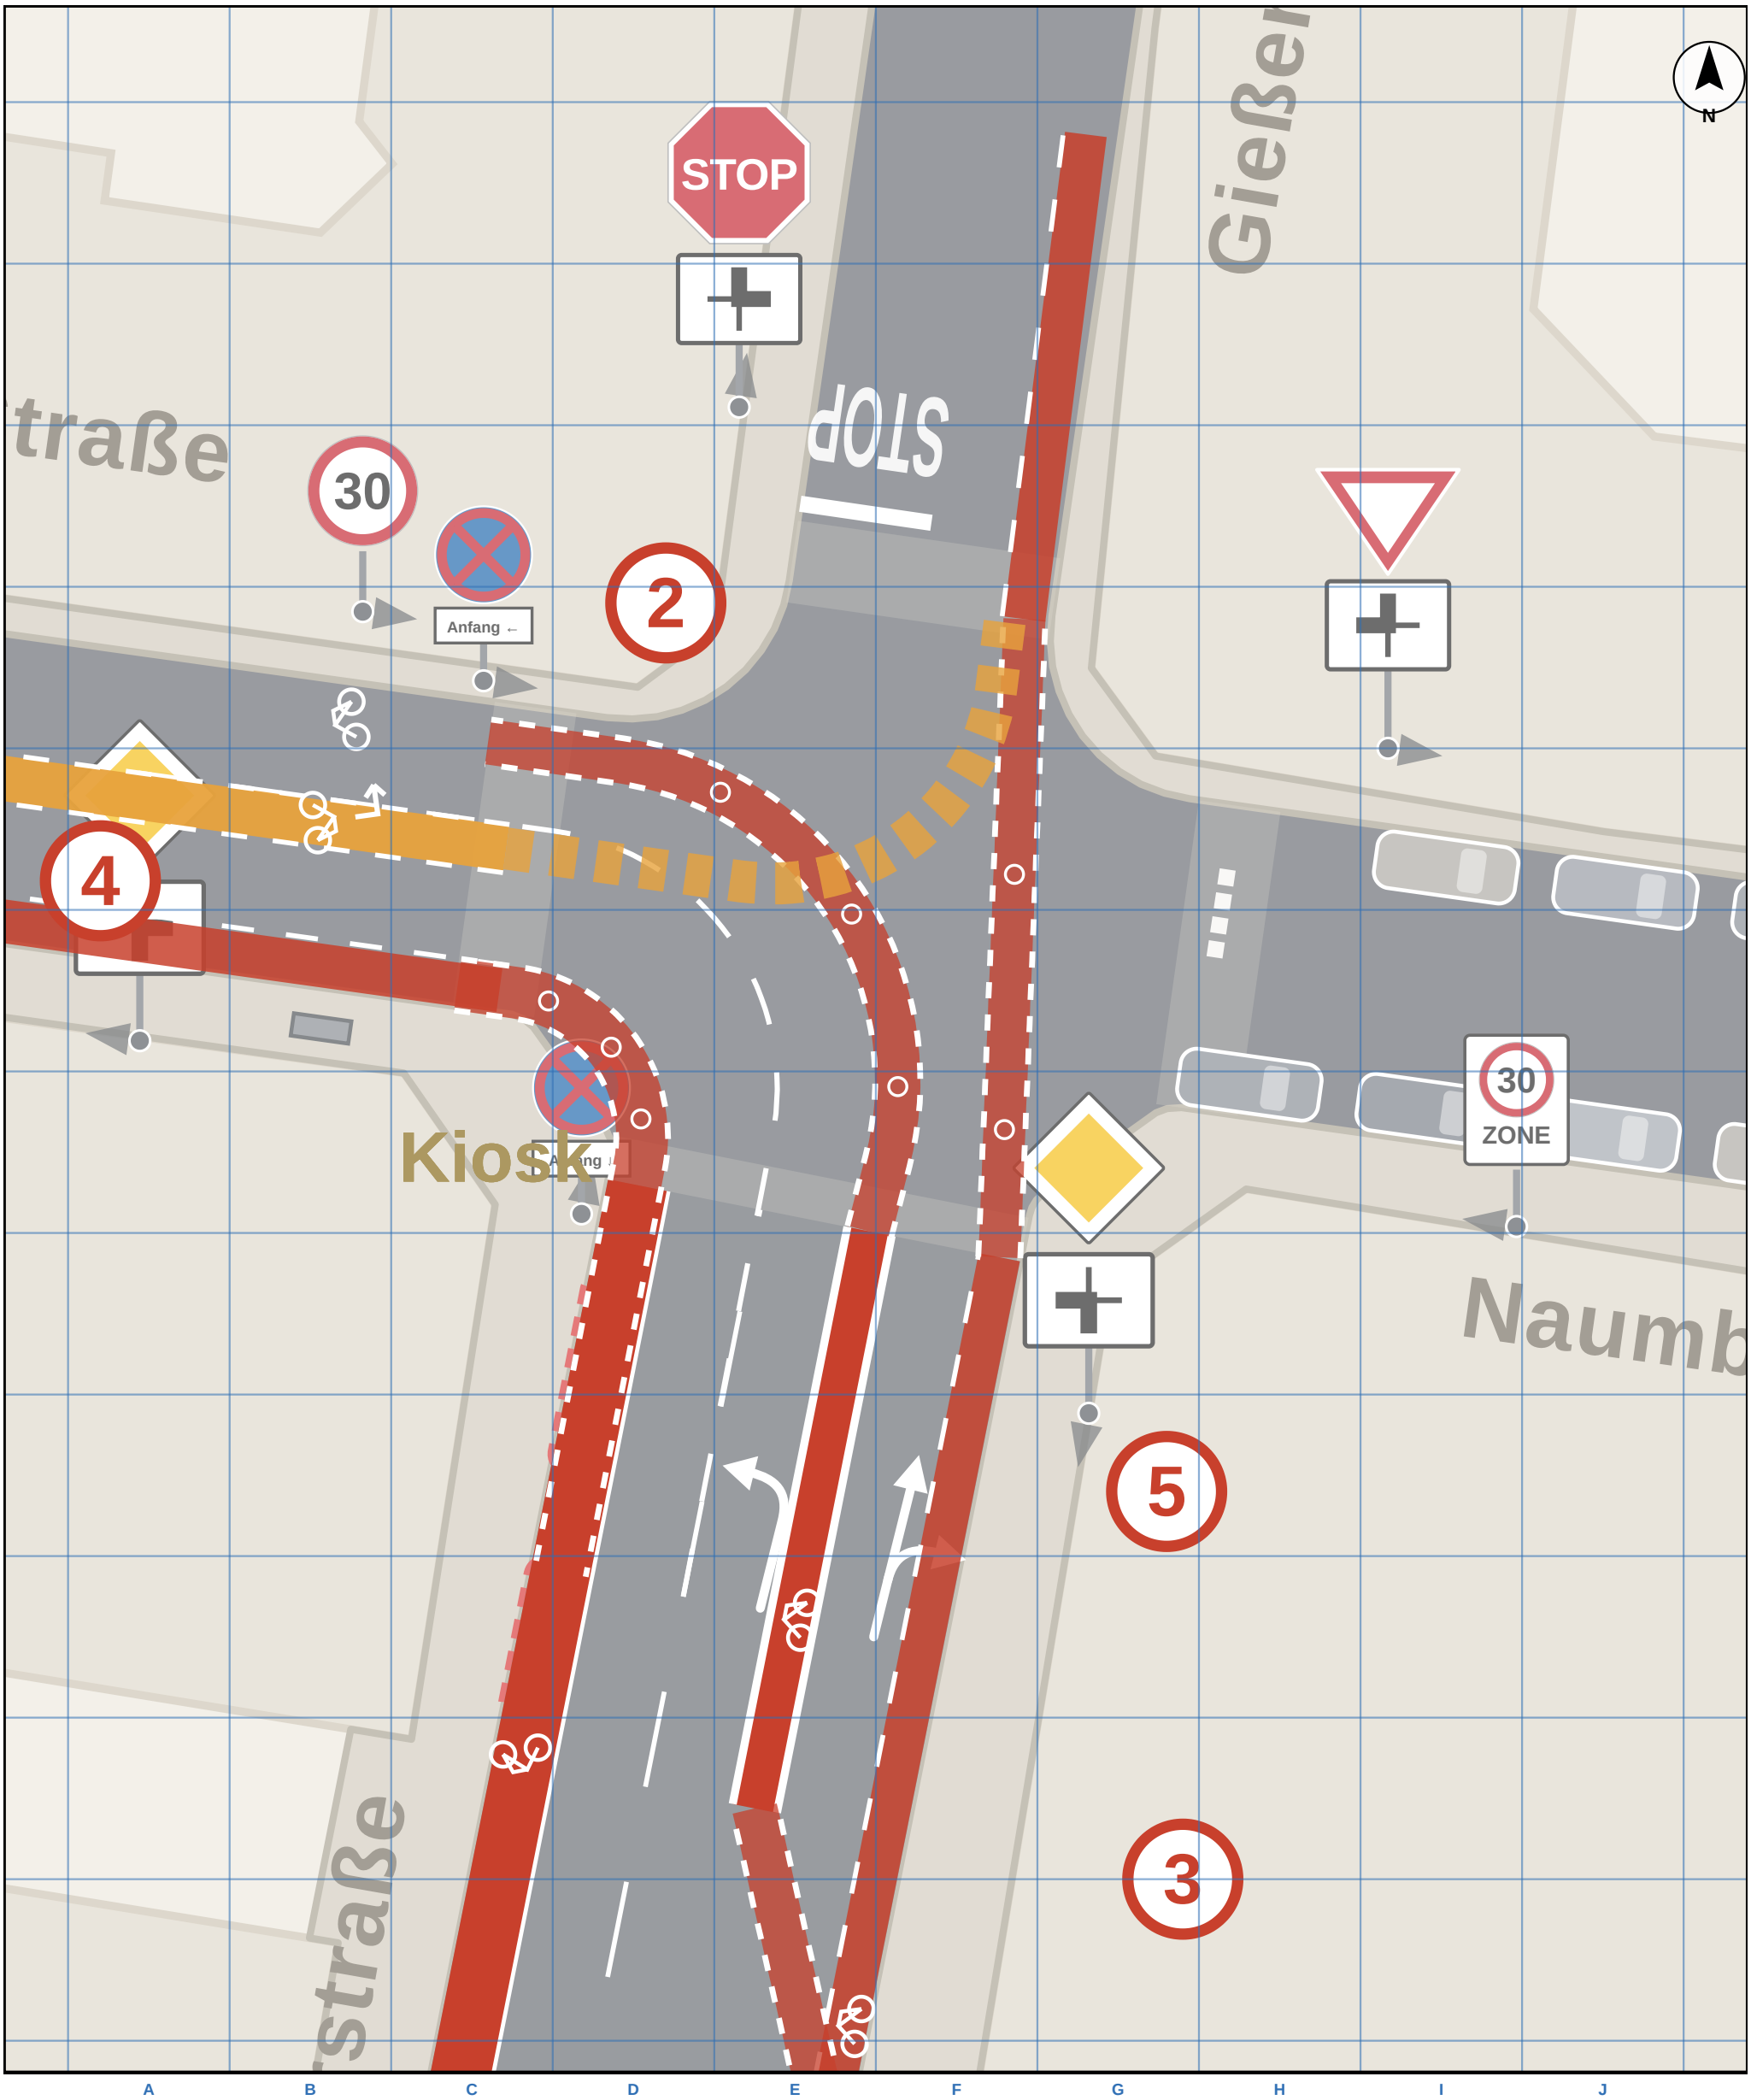

Vorschlag 2 (Weiterentwicklung von Vorschlag 1 nach der Simulation, Lage ca. ±0,5 m)
1 wie Vorschlag 1: Schutzstreifen West ostwärts, Furt um die Kiosk-Ecke, Radfahrstreifen Süd südwärts
2 Rad Süd nach West im Radstreifen in Mittellage, im Bogen rechts neben den abbiegenden Kfz, danach Mischverkehr Tempo 30 · Rad Süd nach Nord rechts, Furt geradeaus
3 Einfädelung: Rad nach West wechselt früh und markiert in die Mittellage · 4 Aufstellstreifen Rad West nach Nord
5 zwei Kfz-Spuren nach Norden bleiben (links / geradeaus und rechts), schmaler: 2,75 m, Mittellage 1,4 m, Schutzstreifen 1,3 m