
Kreuzung Gießerstraße / Naumburger Straße, Leipzig-Plagwitz

Vorschlag 1 der Initiative · Gesamtplan · Maßstab 1:400 bei Druck auf A3 · Raster 10 m · Stand 18.10.2026 · Seite 1 von 2

Radführung entlang der abknickenden Vorfahrt, eine Kfz-Spur nach Norden. Rot = Radverkehr, orange = Rad links abbiegen West nach Nord. Ergänzungen bitte farbig einzeichnen.

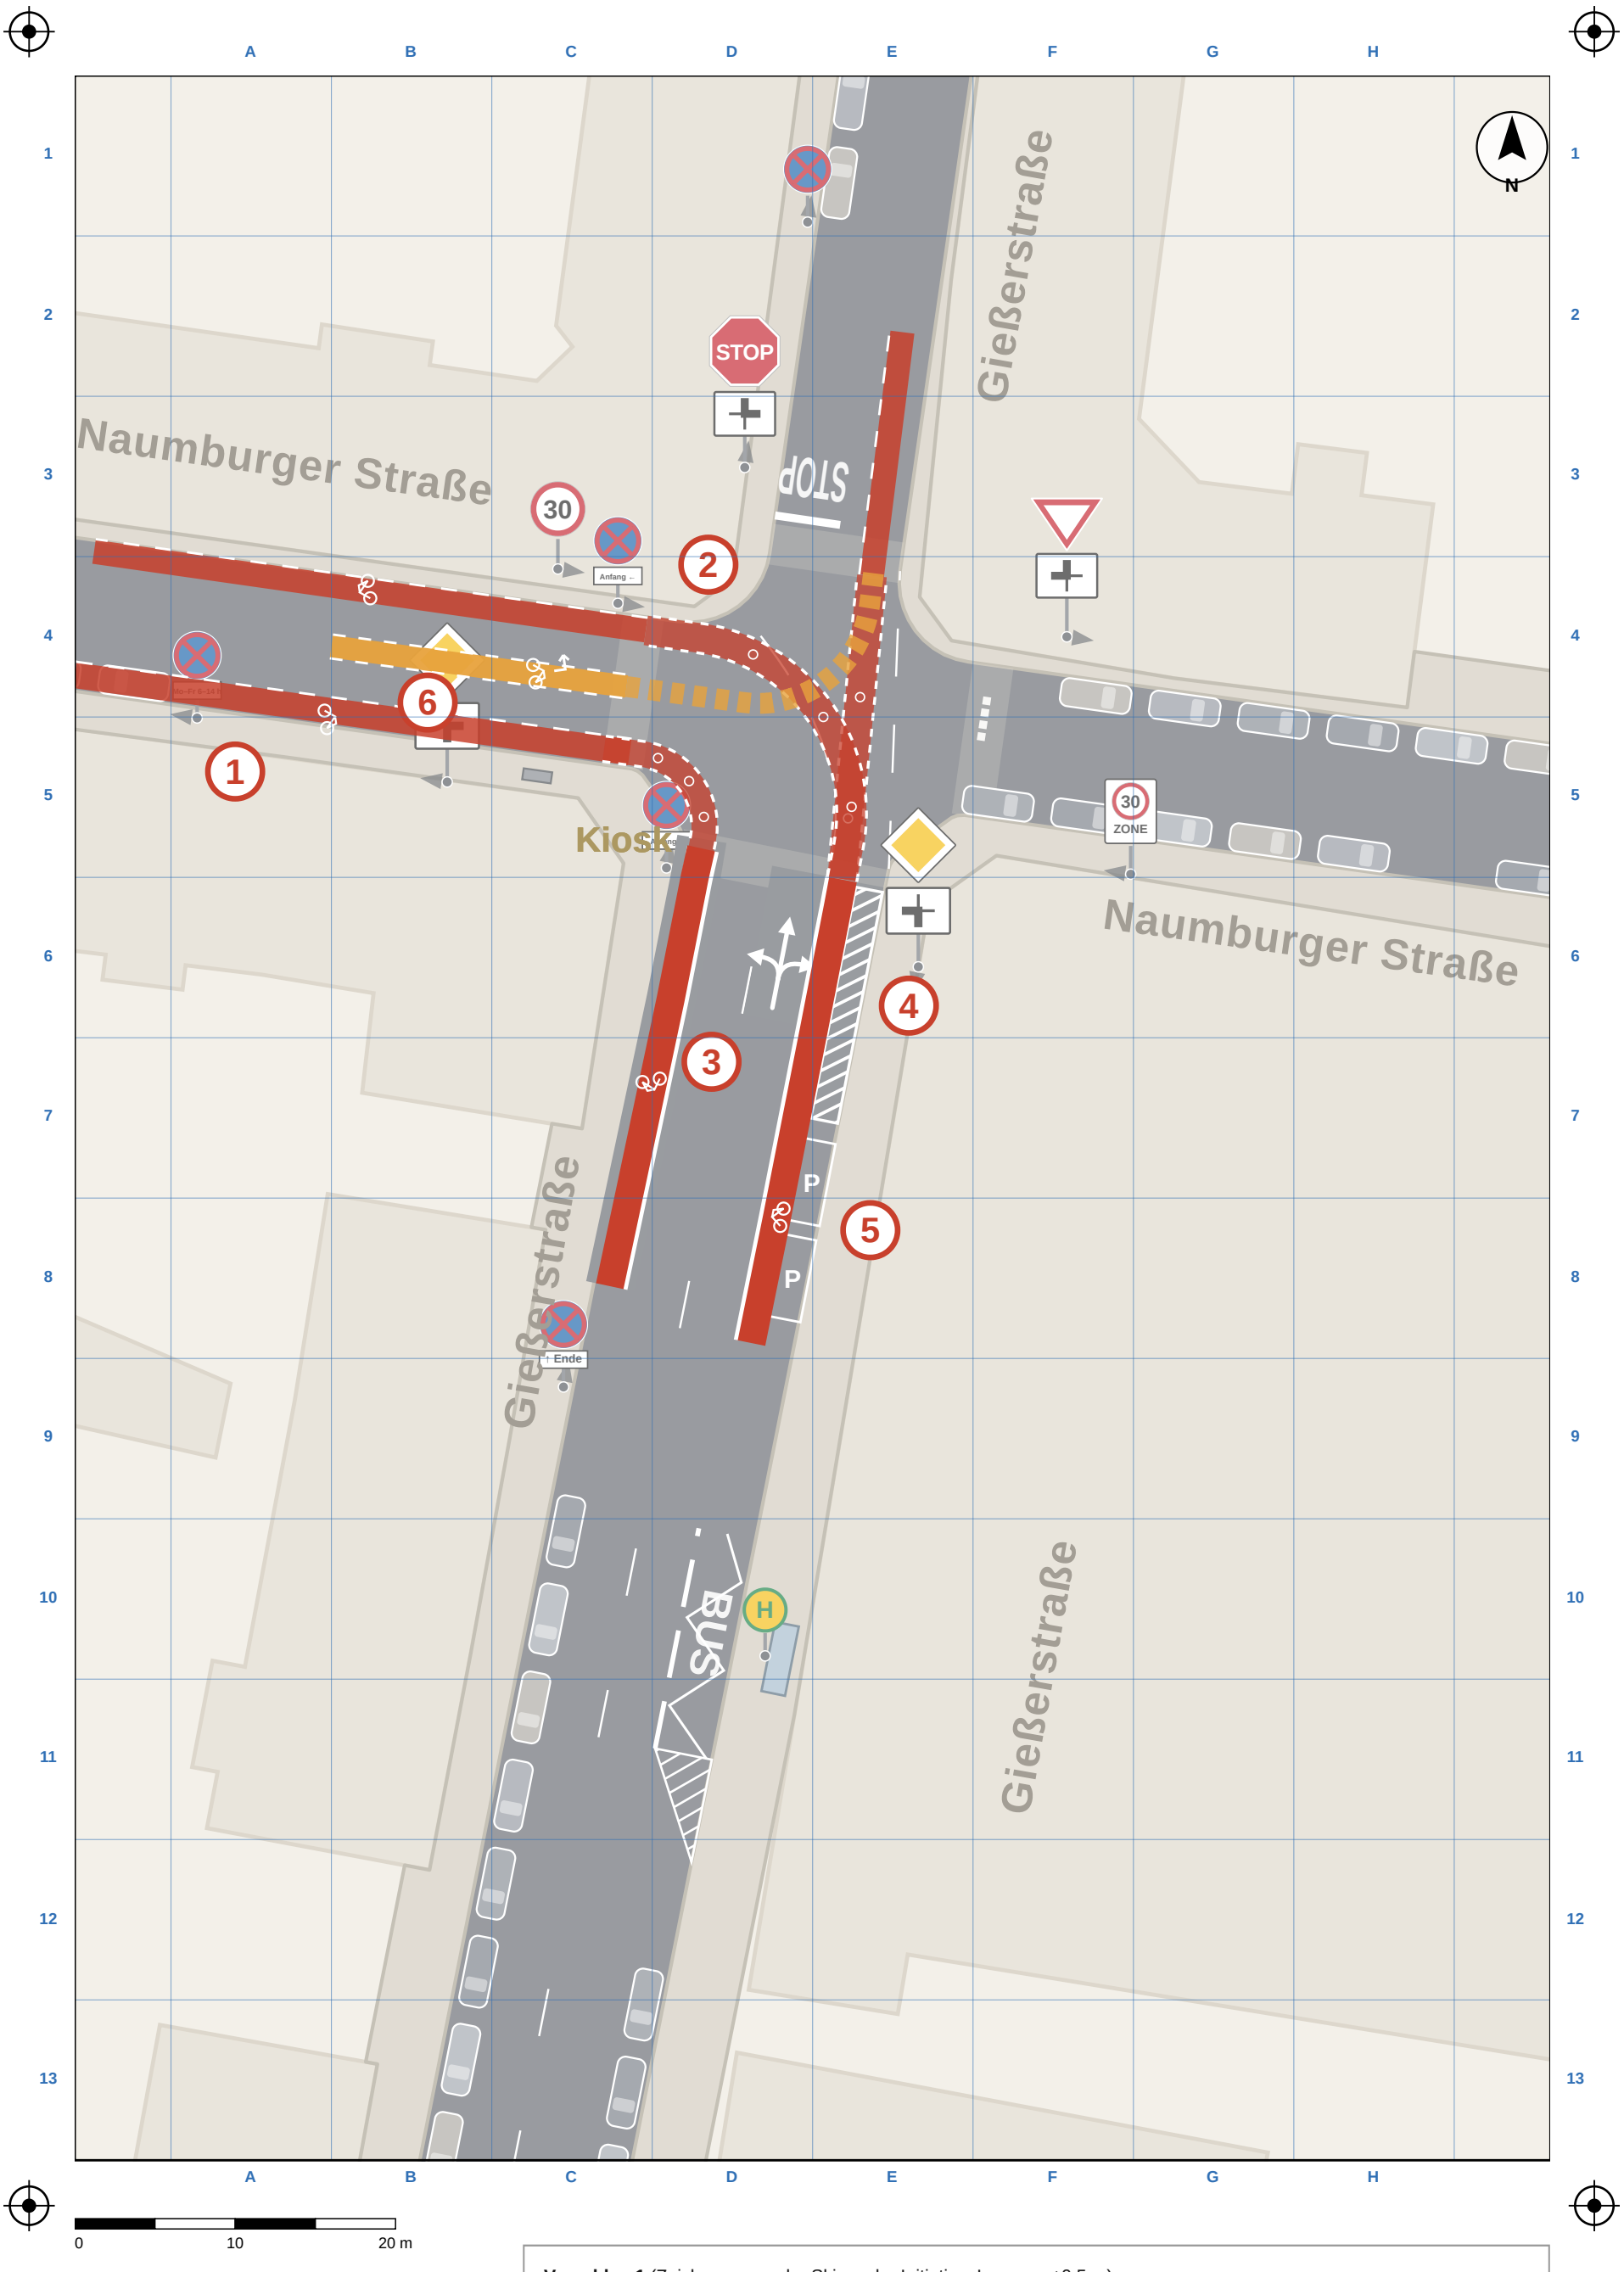

Vorschlag 1 (Zeichnung aus der Skizze der Initiative, Lage ca. ±0,5 m)

- 1 Schutzstreifen West ostwärts, rote Furt um die Kiosk-Ecke, Radfahrstreifen Süd südwärts bis Ende Halteverbot
- 2 Radfahrstreifen Süd nordwärts, Furt geradeaus nach Nord und im Außenbogen nach West, Schutzstreifen Nord und West


3 eine Kfz-Spur nach Norden (Pfeil links, geradeaus, rechts) · 4 Sperrfläche · 5 zwei Parkplätze

- 6 neu: Aufstellstreifen für Rad links abbiegen West nach Nord mit Furt

Kreuzung Gießerstraße / Naumburger Straße, Leipzig-Plagwitz

Vorschlag 1 der Initiative · Knoten im Detail · Maßstab 1:200 bei Druck auf A3 · Raster 5 m · Stand 18.10.2026 · Seite 2 von 2

Radführung entlang der abknickenden Vorfahrt, eine Kfz-Spur nach Norden. Rot = Radverkehr, orange = Rad links abbiegen West nach Nord. Ergänzungen bitte farbig einzeichnen.

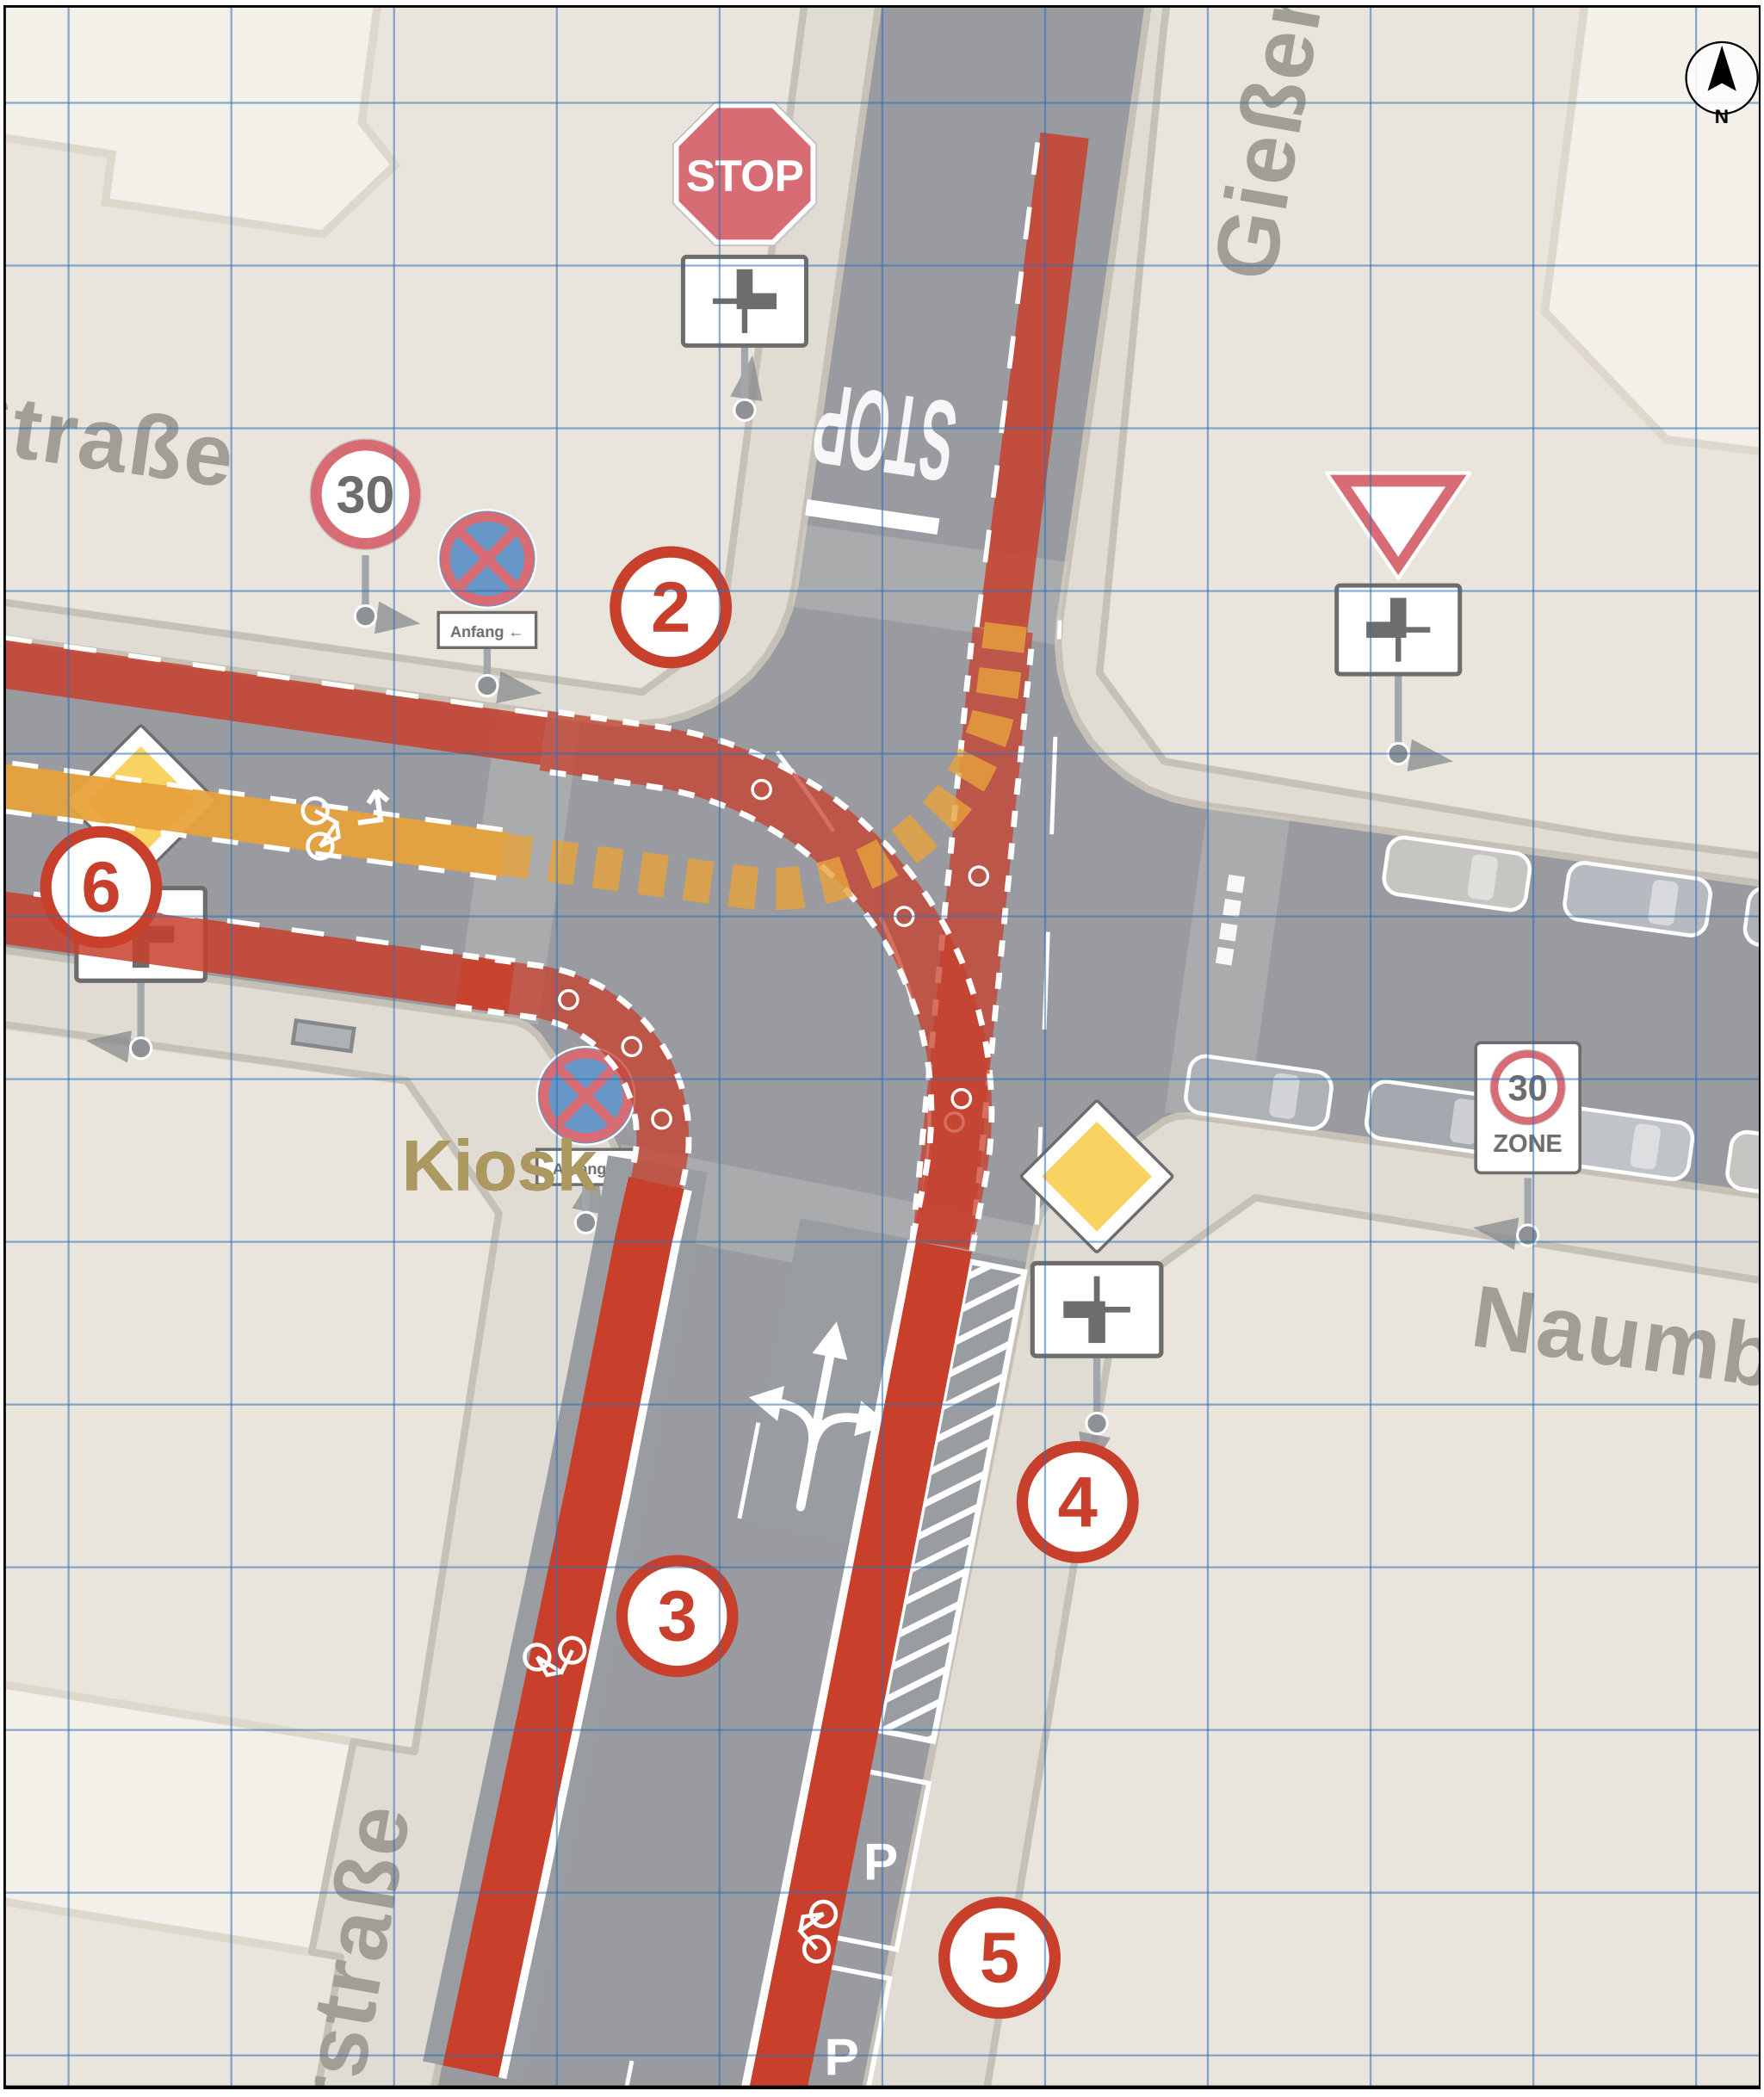

Vorschlag 1 (Zeichnung aus der Skizze der Initiative, Lage ca. ±0,5 m)

- 1 Schutzstreifen West ostwärts, rote Furt um die Kiosk-Ecke, Radfahrstreifen Süd südwärts bis Ende Halteverbot
- 2 Radfahrstreifen Süd nordwärts, Furt geradeaus nach Nord und im Außenbogen nach West, Schutzstreifen Nord und West

3 eine Kfz-Spur nach Norden (Pfeil links, geradeaus, rechts) · 4 Sperrfläche · 5 zwei Parkplätze

- 6 neu: Aufstellstreifen für Rad links abbiegen West nach Nord mit Furt